
CONTOH KONSEPTUAL · BUKAN GAMBAR KERJA / BUKAN UNTUK KONSTRUKSI

INFRASTUKTUR · PUSKESMAS PRAMBANAN

Denah Lantai 1 · Area Pelayanan

Skema awal tata ruang fasilitas kesehatan — bukan hasil survei atau desain arsitek

SIMULASI — Dimensi, luasan, struktur, akses, dan pemenuhan standar belum diverifikasi. Jangan digunakan untuk pembangunan.

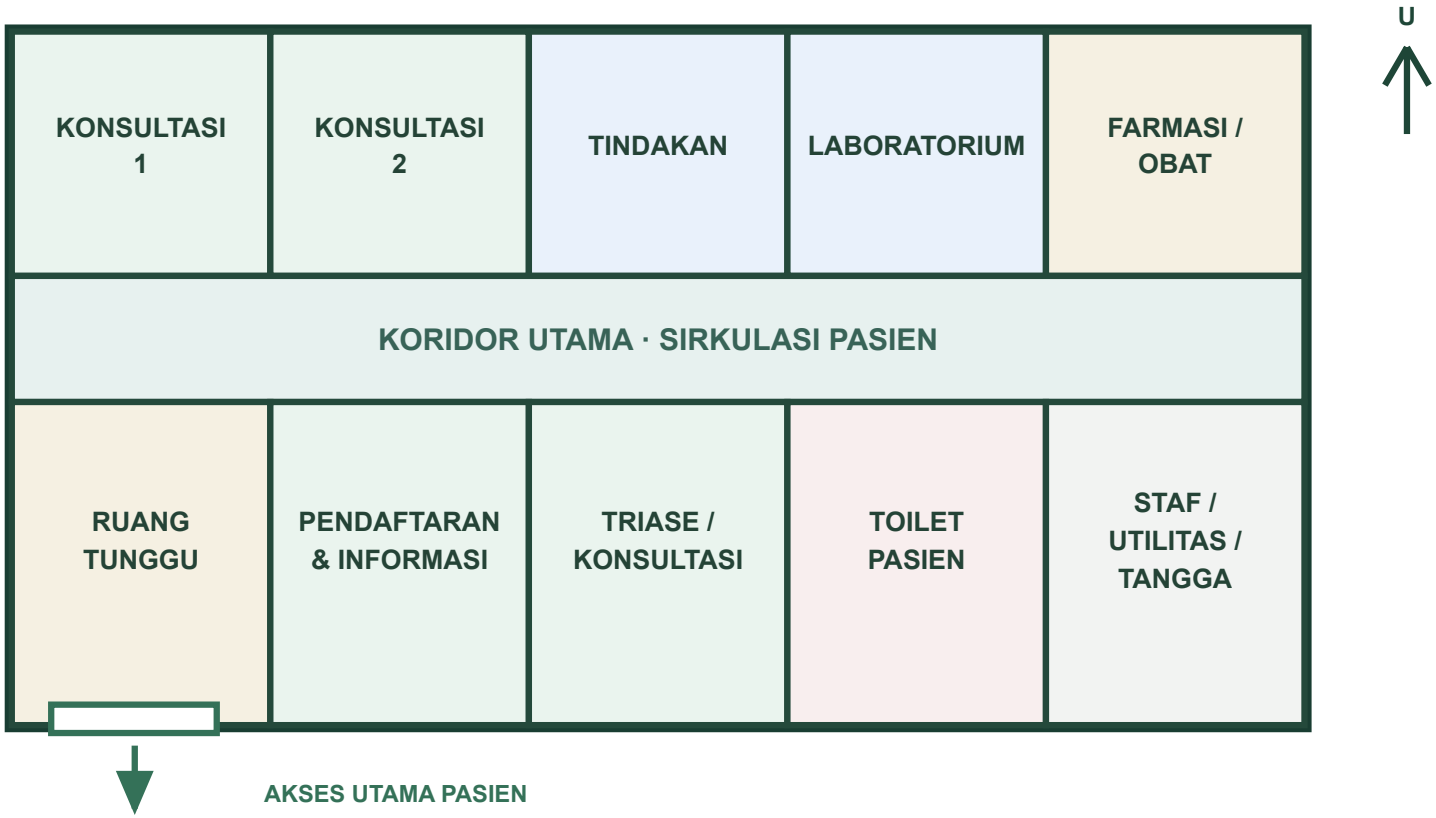

DENAH SKEMATIK · UKURAN RUANG TIDAK BERSKALA

Area klinis | Area publik | Penunjang / akses vertikal | Orientasi utara bersifat ilustratif

CONTOH SIMULASI · Rancangan bukan dokumen arsitektur, struktur, PBG, atau gambar pelaksanaan. Wajib dirancang dan diverifikasi tenaga ahli berwenang.

CONTOH KONSEPTUAL · BUKAN GAMBAR KERJA / BUKAN UNTUK KONSTRUKSI

INFRASTUKTUR · PUSKESMAS PRAMBANAN

Denah Lantai 2 · Area Pengelola

Skema awal ruang administrasi dan staf — dapat berubah setelah kebutuhan ruang disusun

SIMULASI — Jumlah lantai dua hanya asumsi dari narasi proyek; gambar ini bukan kondisi terbangun atau desain yang disetujui.



DENAH SKEMATIK · UKURAN RUANG TIDAK BERSKALA · *JALUR EVAKUASI WAJIB DIKAJI AHLI


Administrasi | Ruang staf | Koridor dan tangga | Orientasi utara ilustratif

CONTOH SIMULASI · Tata ruang, aksesibilitas, keselamatan kebakaran, struktur, dan seluruh dimensi wajib dihitung serta disetujui tenaga ahli berwenang.

VISUALISASI KONSEPTUAL

Tampak luar Puskesmas Prambanan

Ilustrasi eksterior sebagai pelengkap denah bangunan

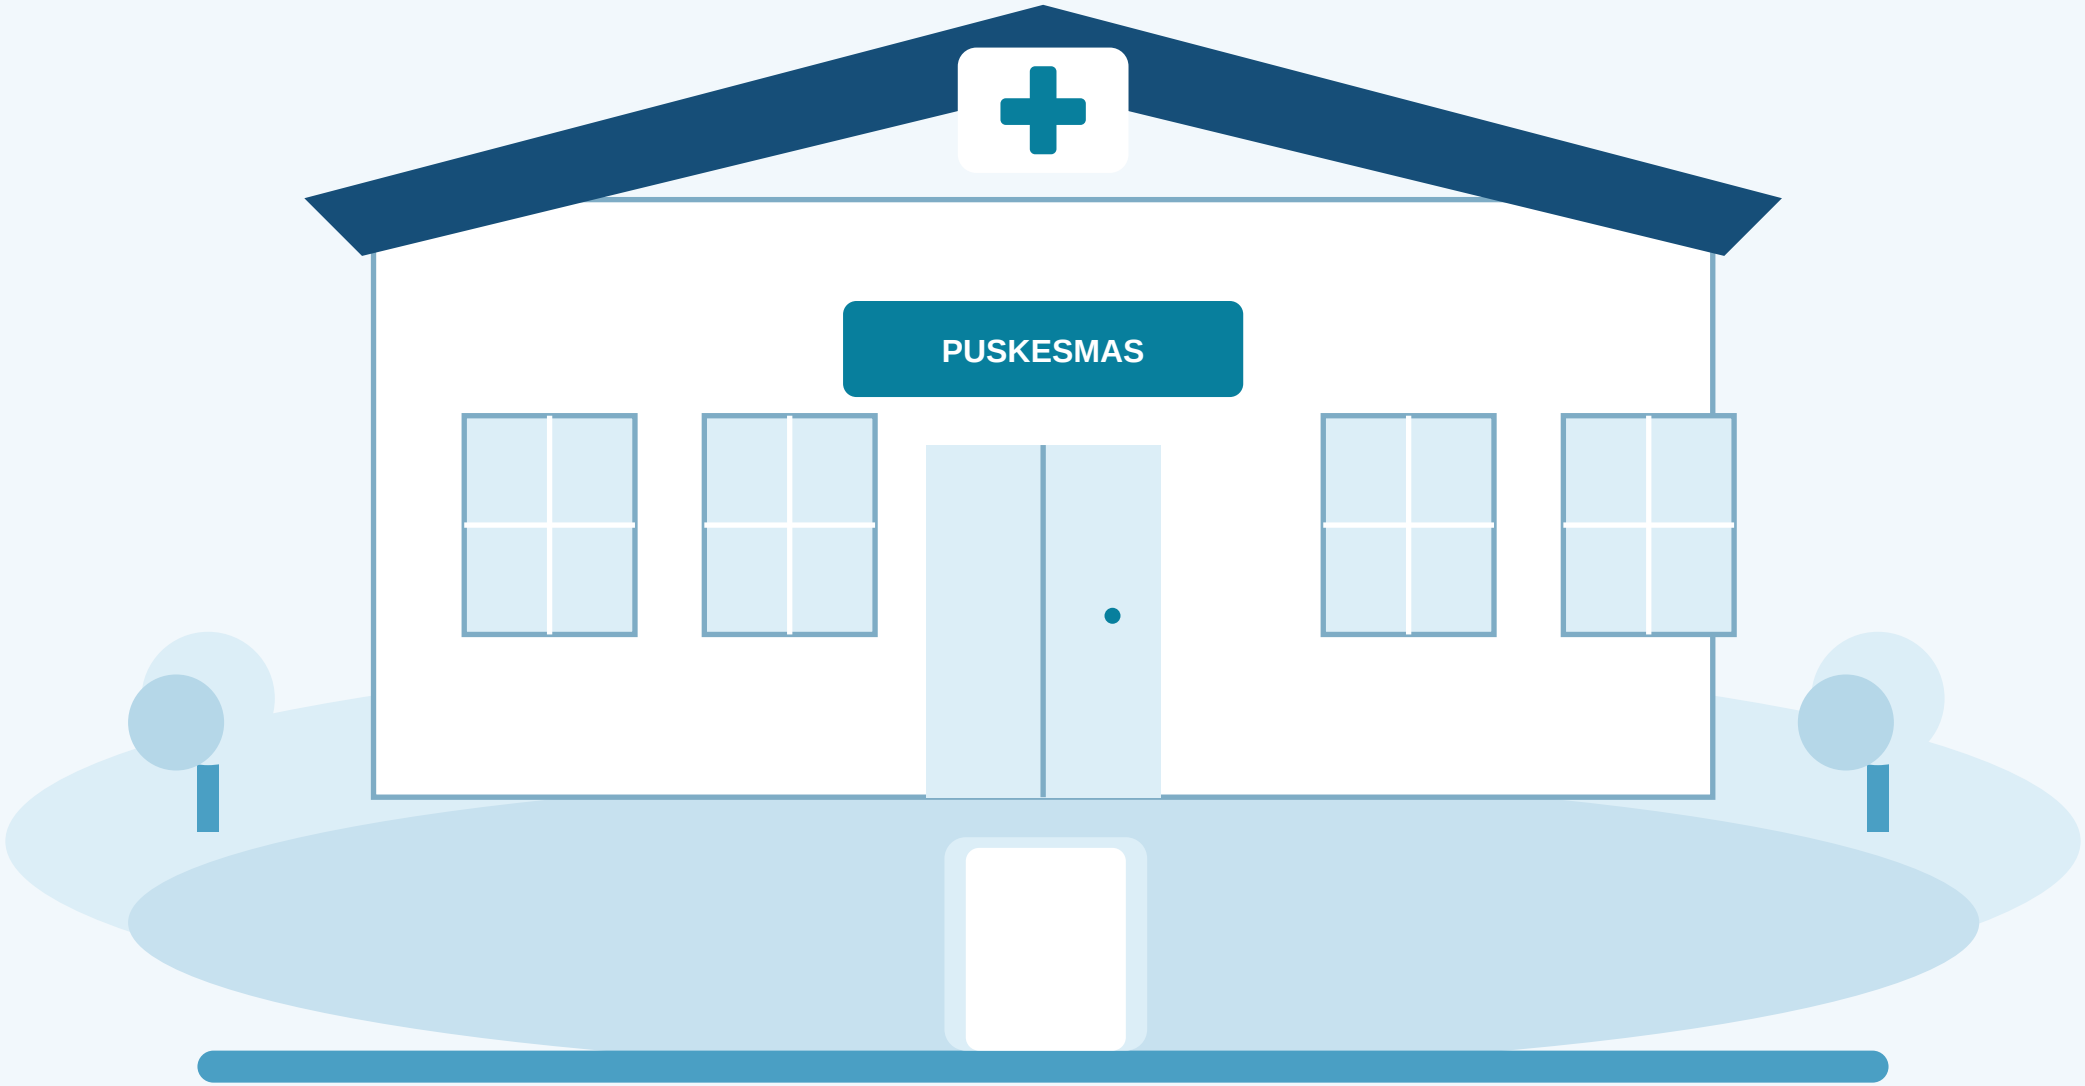

CATATAN Ilustrasi konseptual, bukan gambar kerja atau visualisasi final.